

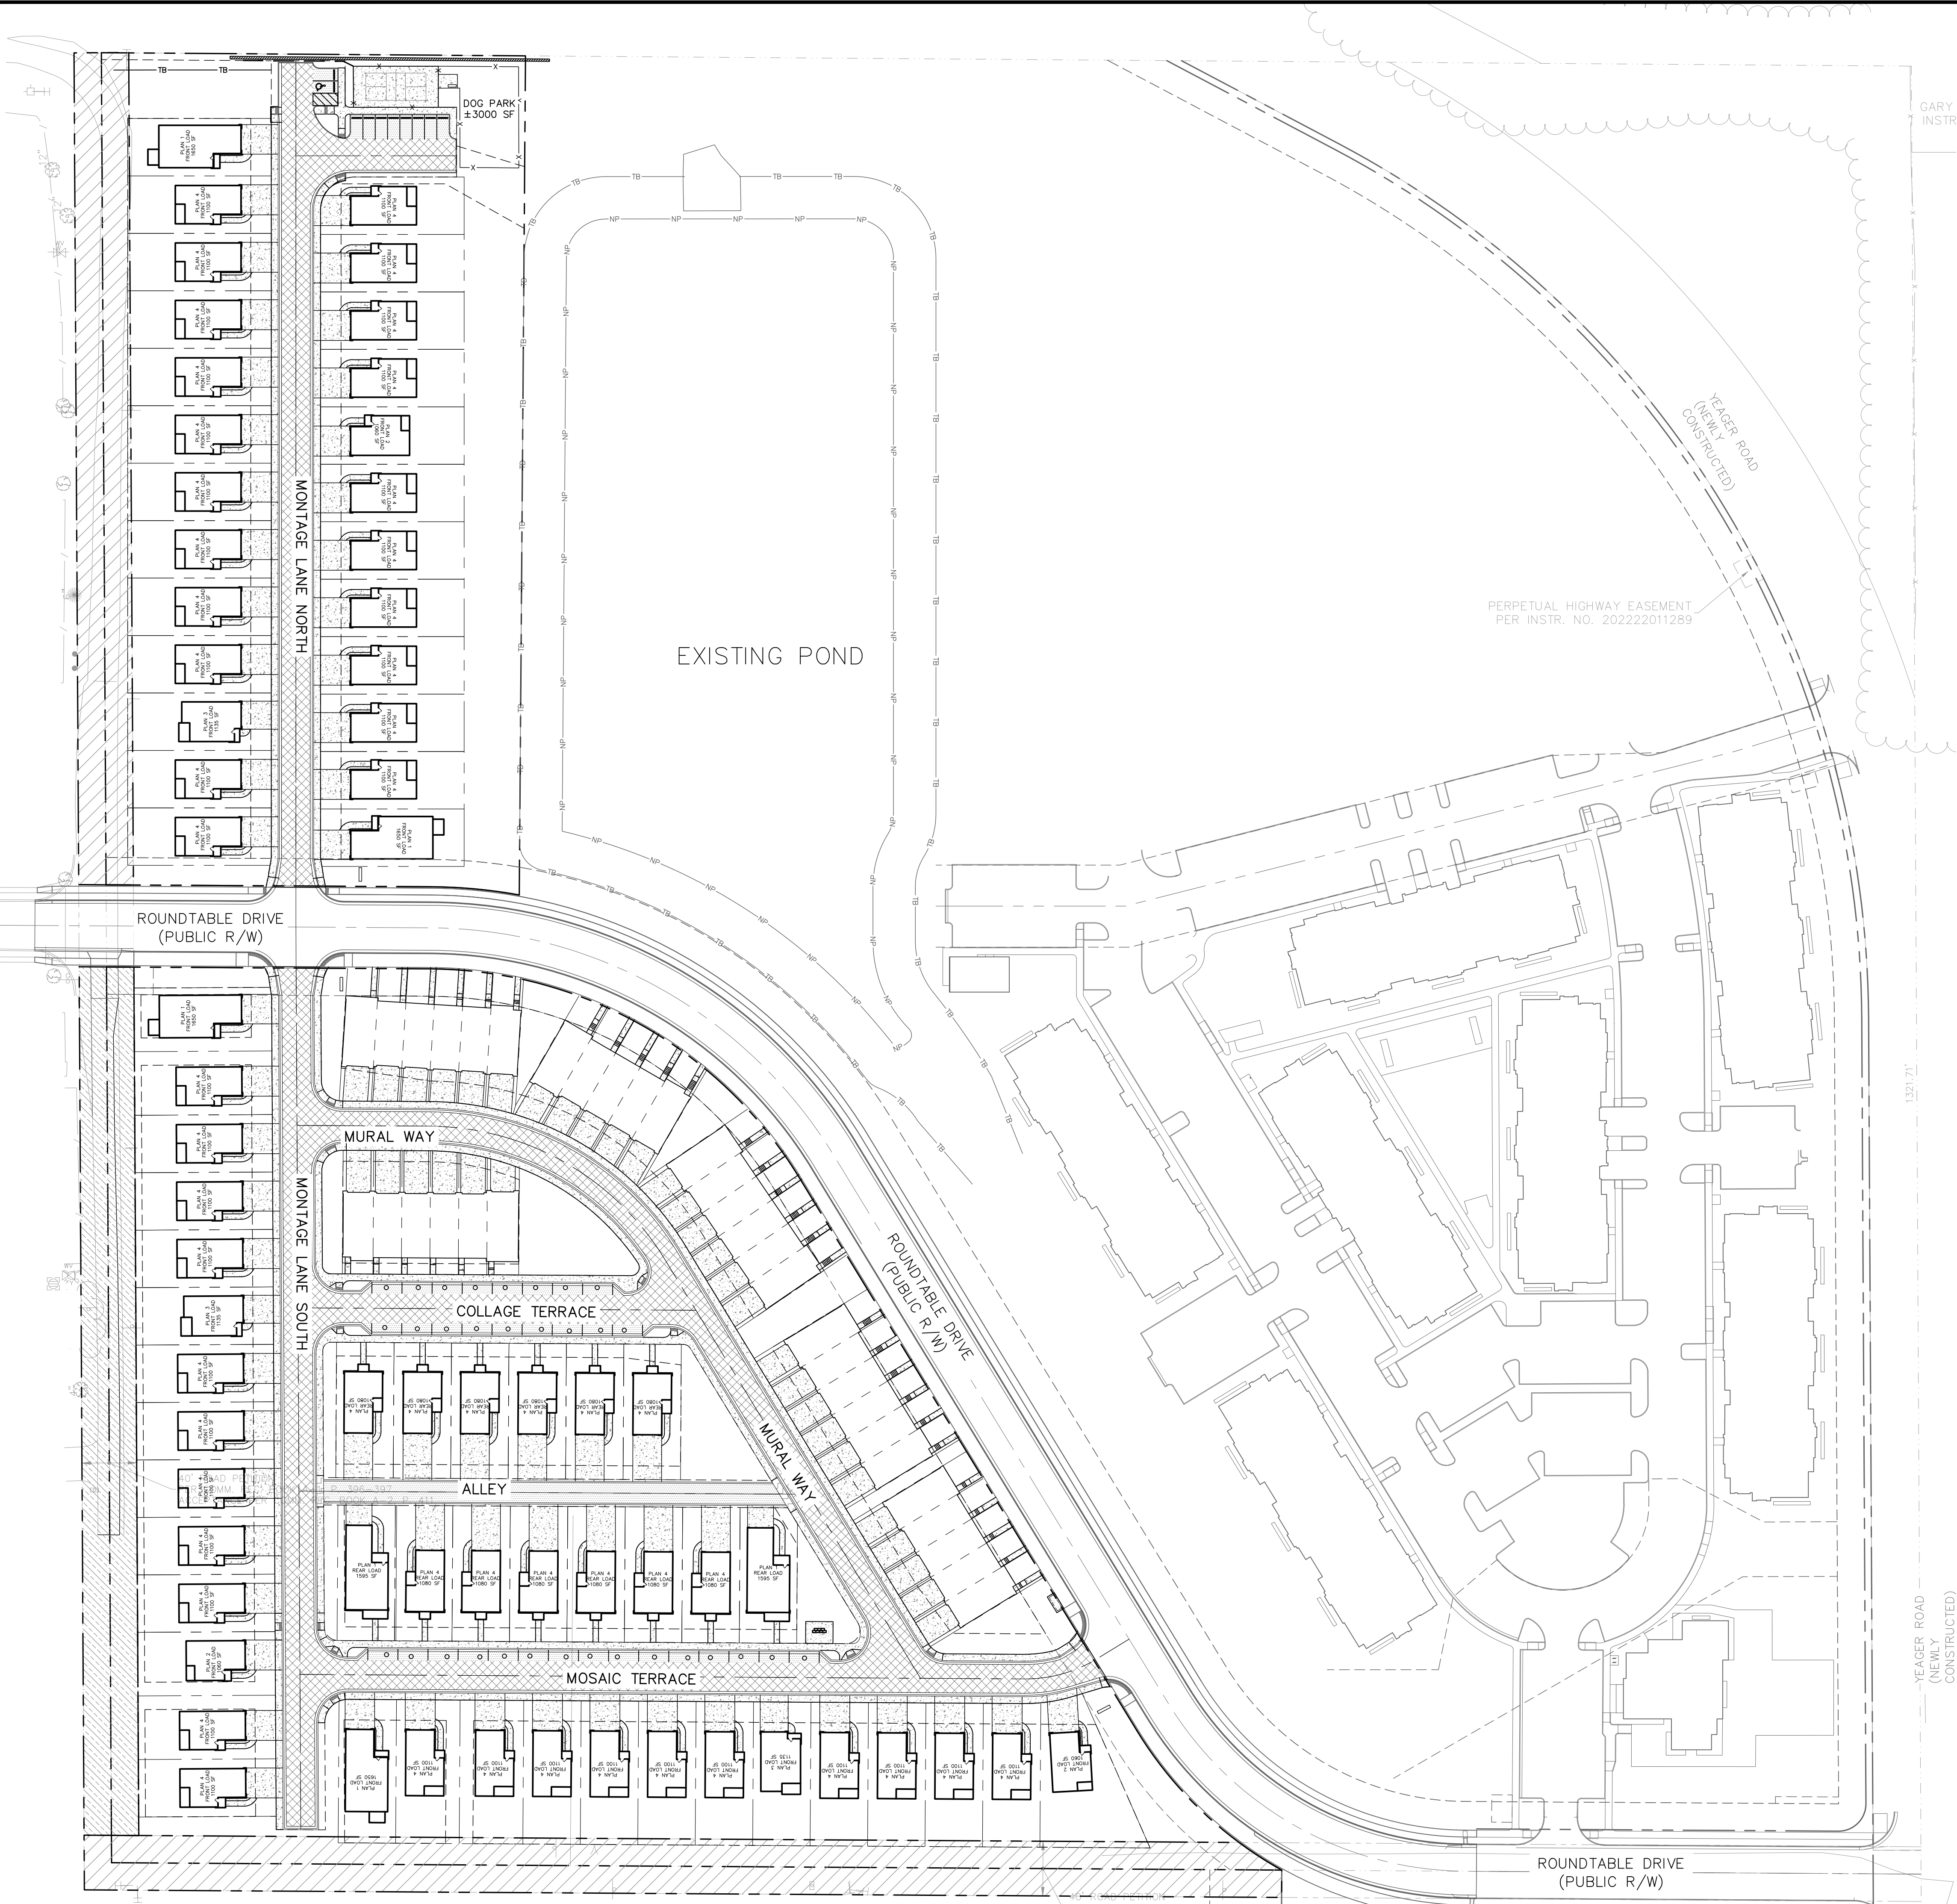


Drawing name: K:\WF_LDEV\170291013_Buckingham\Bogor Phase 3_MLF_INV2 Design\CADD\PlanSheets\C300-OVERALL SITE PLAN.dwg C300 Oct 03, 2025 10:49am by: Carson,Emily
This document, together with the concepts and designs presented herein, as an instrument of service, is intended only for the specific purpose and client for which it was prepared. Reuse of and improper reliance on this document without written authorization and adaptation by Kimley-Horn and Associates, Inc. shall be without liability to Kimley-Horn and Associates, Inc.

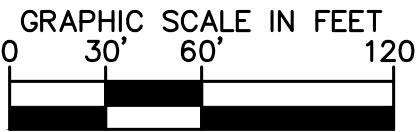

Indiana Utilities Protection Service

Call 811
before you dig

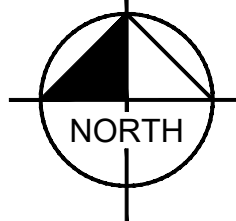

EXISTING LEGEND

BOLLARD	MISC LID	YARD LIGHT
CONTROL BENCHMARK	MONITOR WELL	SANITARY CLEANOUT
ROW MONUMENT	GAS MARKER	SANITARY MANHOLE
FLAG POLE	GAS METER	VENT PIPE
MAIL BOX	GAS VALVE	STORM CURB INLET
UTILITY POLE	AC UNIT	STORM INLET
POST	AREA LIGHT	STORM ROOF DRAIN
SOIL BORING	ELECTRICAL BOX	STORM DRAIN MANHOLE
HANDICAP SYMBOL	ELECTRICAL HAND HOLE	STORM YARD DRAIN
SIGN	ELECTRICAL METER	FIRE DEPT CONNECTION
CABLE MANHOLE	ELECTRICAL MANHOLE	FIRE HYDRANT
CABLE PEDESTAL	ELECTRICAL MARKER	IRRIGATION VALVE
TELEPHONE PEDESTAL	ELECTRICAL TRANSFORMER	POST INDICATOR VALVE
TELEPHONE HAND HOLE	GUY POLE/WIRE	WELL
TELEPHONE MARKER	POWER POLE	WATER METER
TELEPHONE MANHOLE	TRAFFIC SIGNAL POLE	WATER VALVE
FIBER OPTIC MARKER	TRAFFIC MANHOLE	TREE / STUMP
SWALE	TOE OF SLOPE	
FENCE LINE	TOP OF BANK	
SS	UNDERGROUND FIBER OPTIC	
SD	OVERHEAD ELECTRICAL	
W	UNDERGROUND GAS	
TREE LINE	UNDERGROUND TELEPHONE	

PAVING LEGEND

	STANDARD DUTY ASPHALT PAVEMENT SEE CONSTRUCTION DETAILS FOR PAVEMENT SECTION
	HEAVY DUTY ASPHALT PAVEMENT SEE CONSTRUCTION DETAILS FOR PAVEMENT SECTION
	CONCRETE SIDEWALK/DRIVEWAY SEE CONSTRUCTION DETAILS FOR PAVEMENT SECTION
	APPROXIMATE EXTENTS OF EXISTING ROADWAY PAVEMENT TO BE REMOVED BY TIPPECANOE COUNTY HIGHWAY
	RIGHT-OF-WAY TO BE VACATED FOLLOWING ROUNDTABLE DRIVE COMPLETION AND ACCEPTANCE BY TIPPECANOE COUNTY

SITE SUMMARY

SITE ZONING	=	R1+R3 TO PDORS
SITE ACREAGE	=	+13.4 AC.
GREENSPACE	=	+49.5%
BUILDING COVERAGE	=	+20.3%
ON-STREET PARKING SPACES (STANDARD) PROVIDED	=	32 SPACES
AMENITY AREA PARKING SPACES (STANDARD) PROVIDED	=	10 SPACES
PARKING SPACES (ACCESSIBLE) PROVIDED	=	1 SPACES
IN-UNIT GARAGES PROVIDED	=	100 GARAGES
TOTAL PARKING SPACES PROVIDED	=	42 SPACES
TOTAL GARAGE SPACES PROVIDED	=	200 GARAGES

Kimley-Horn

©2025 KIMLEY-HORN AND ASSOCIATES, INC.
101 LAFAYETTE, IN 47906
WWW.KIMLEY-HORN.COM

AS NOTED

DESIGNED BY MAP GME

DRAWN BY: DAK BAG HAS

CHECKED BY: JAN

REGISTERED PROFESSIONAL ENGINEER

No. PE10606558

STATE OF INDIANA

Joshua A. Hixon

BUCKINGHAM

CORTANES

OVERALL SITE PLAN

RESEARCH VILLAGE PHASE 3

ORIGINAL ISSUE: 09/12/2025

KHA PROJECT NO. 170291013

SHEET NUMBER C300